PÔDORYS 1.NP

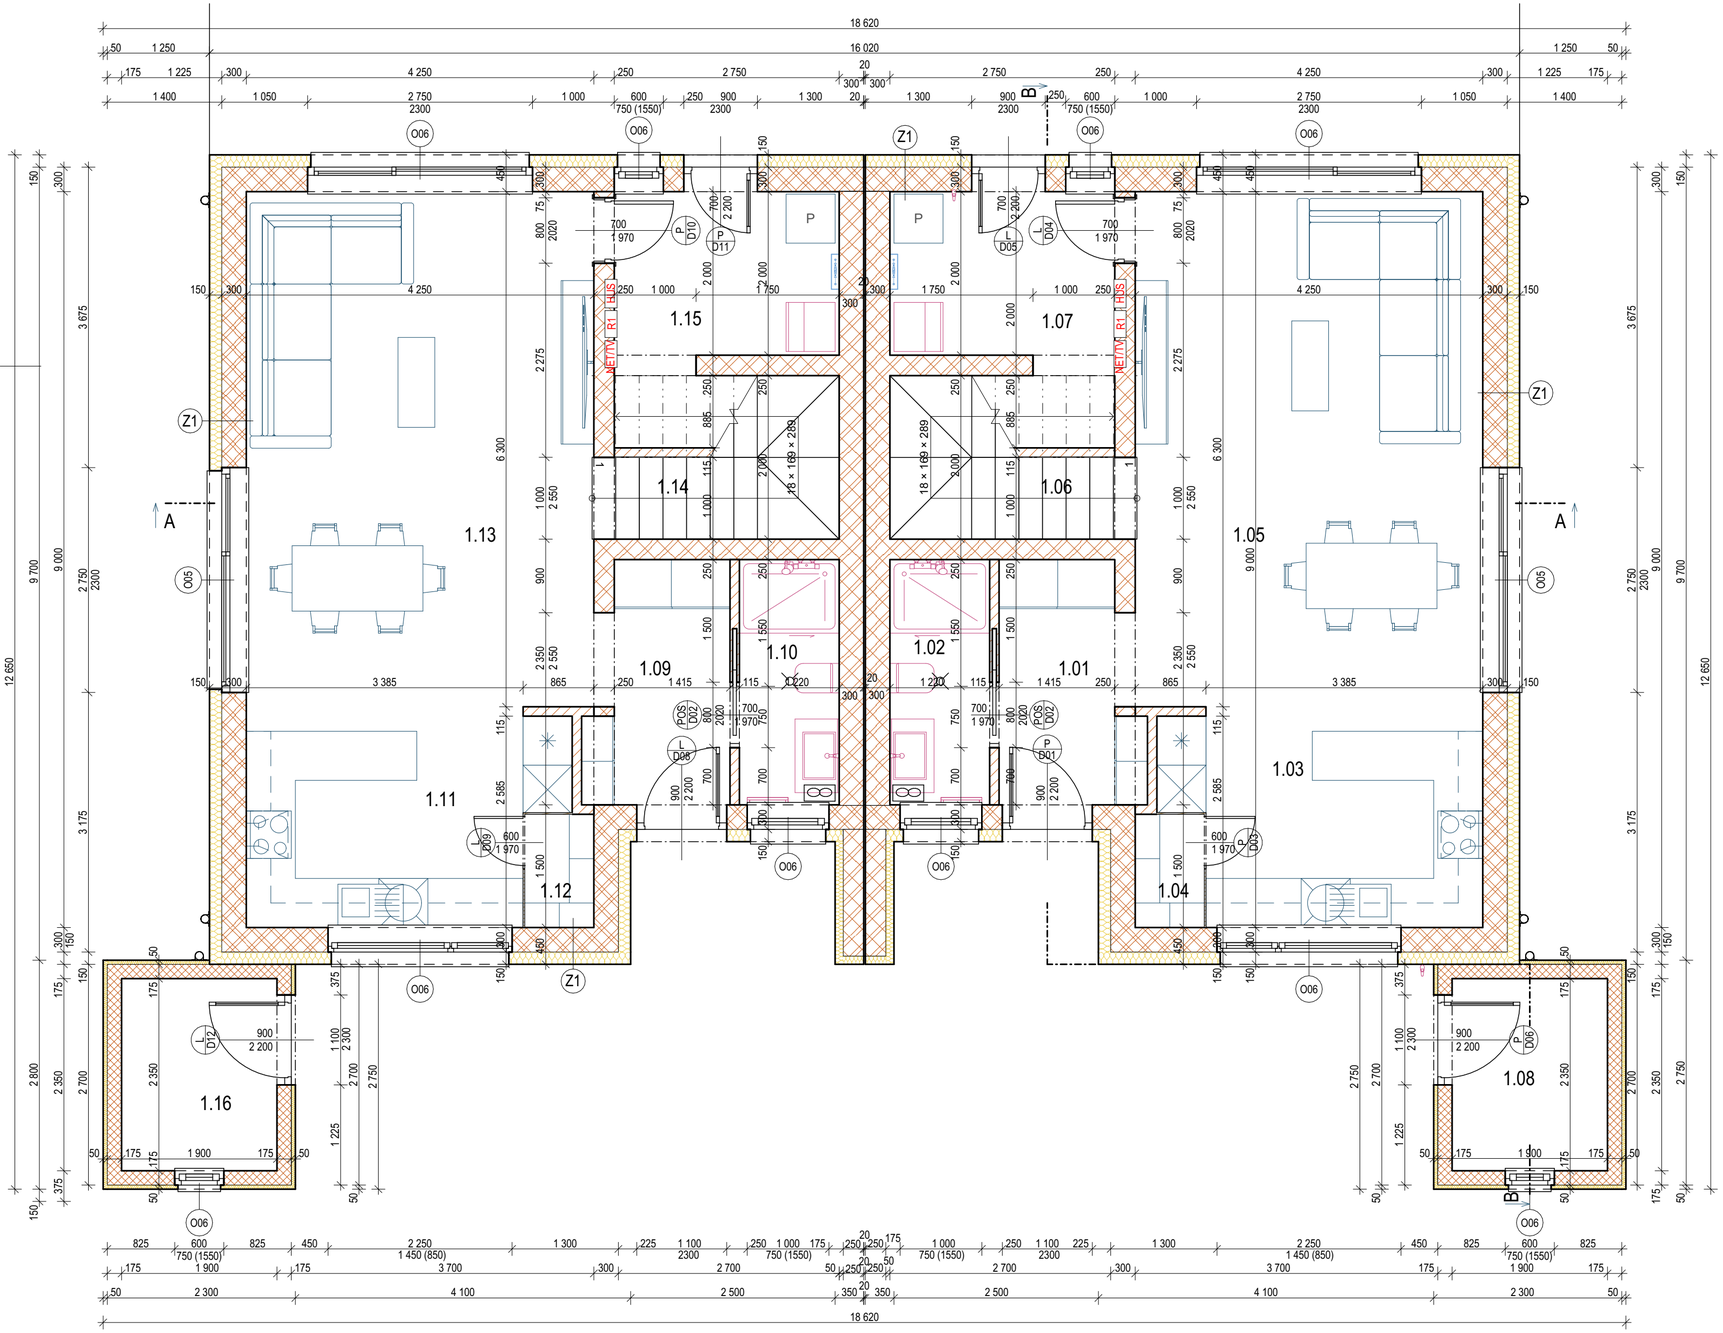

LEGENDA MIESTNOSTÍ 1.NP

OBJEKT	Č.M.	NÁZOV MIESTNOSTI	PLOCHA(m²)	PODLAHA		STENY	STROP	POZN.
SO01	1.01	ZÁDVERIE	4,92	GRESOVÁ DLAŽBA	P1	SÁDROVÁ OMIETKA	SDK PODHĽAD	v=2700mm
	1.02	KÚPEĽŇA	3,66			GRESOVÝ OBKLAD		
	1.03	KUCHYŇA	9,14	PLÁVAJÚCA PODLAHA		SÁDROVÁ OMIETKA		
	1.04	SKLAD	1,17					
	1.05	OBÝVACIA IZBA + JEDÁLEŇ	26,78					
	1.06	SCHODISKO	6,00	DREVENÁ PODLAHA	P2			
	1.07	TECHNICKÁ MIESTNOSŤ	9,49	GRESOVÁ DLAŽBA	P1			
	1.08	SKLAD	4,47	GRESOVÁ DLAŽBA			OSB DOSKY	v=2775mm
SO02	1.09	ZÁDVERIE	4,92	GRESOVÁ DLAŽBA	P1	SÁDROVÁ OMIETKA	SDK PODHĽAD	v=2700mm
	1.10	KÚPEĽŇA	3,66			GRESOVÝ OBKLAD		
	1.11	KUCHYŇA	9,14	PLÁVAJÚCA PODLAHA		SÁDROVÁ OMIETKA		
	1.12	SKLAD	1,17					
	1.13	OBÝVACIA IZBA + JEDÁLEŇ	26,78					
	1.14	SCHODISKO	6,00	DREVENÁ PODLAHA	P2			
	1.15	TECHNICKÁ MIESTNOSŤ	9,49	GRESOVÁ DLAŽBA	P1			
	1.16	SKLAD	4,47				OSB DOSKY	v=2775mm

SO01		SO02		DVOJDOM	
ZASTAVANÁ PLOCHA 1.NP	81,98m²	ZASTAVANÁ PLOCHA 1.NP	81,98m²	ZASTAVANÁ PLOCHA 1.NP	164,16m²
ÚŽITKOVÁ PLOCHA 1.NP	65,63m²	ÚŽITKOVÁ PLOCHA 1.NP	65,63m²	ÚŽITKOVÁ PLOCHA 1.NP	131,26m²
OBYTNÁ PLOCHA 1.NP	26,78m²	OBYTNÁ PLOCHA 1.NP	26,78m²	OBYTNÁ PLOCHA 1.NP	53,56m²

LEGENDA HORIZONTÁLNYCH KONŠTRUKCIÍ

SKLADBA	VÝZNAM
Z1	1. VONKAJŠIA SILIKÓNOVÁ OMIETKA, hr. 2mm
	2. PENETRAČNÝ NÁTER
	3. VYSTUŽENÁ VRSTVA LEPIDLA SO SKLOTEXTÍLNOU MRIEŽKOU, hr. 18mm
	4. FASÁDNA MINERÁLNA VLNA, hr. 150mm
	5. KERAMICKÉ TVÁRNICE POROTHERM 30 KOMBI PROFI DRYFIX (250x300x249) hr.300mm
	6. PENETRAČNÝ NÁTER
	7. SÁDROVÁ OMIETKA, hr. 20mm

LEGENDA MATERIÁLOV

GRF. ZN.	MATERIÁL
	OBVODOVÉ KERAMICKÉ TVÁRNICE POROTHERM 30 KOMBI PROFI DRYFIX (250x300x249), hr. 300mm, TR. PEVNOSTI P15, λ=0,165W/m.K, R=2,03 m².K/W, PRVÁ RADA NA MUR. MALTU hr. 12 mm, LEPENÉ NA MUR. PENU DRYFIX
	VNÚTORNÉ KERAMICKÉ TVÁRNICE POROTHERM 25 PROFI DRYFIX (375x250x249) hr. 250mm, TR. PEVNOSTI P12-P15, λ=0,35W/m.K, R=1,11 m².K/W, PRVÁ RADA NA MUR. MALTU hr. 12 mm, LEPENÉ NA MUR. PENU DRYFIX
	VNÚNOTRNÉ KERAMICKÉ TVÁRNICE POROTHERM 17,5 PROFI DRYFIX (375x175x249) hr. 175mm, λ=0,22 W/m.K, R=0,81 m².K/W, PRVÁ RADA NA MUR. MALTU hr. 12 mm, LEPENÉ NA MUR. PENU DRYFIX
	VNÚNOTRNÉ KERAMICKÉ TVÁRNICE POROTHERM 11,5 PROFI DRYFIX (500x115x249) hr. 115mm, λ=0,20 W/m.K, R=0,60 m².K/W, PRVÁ RADA NA MUR. MALTU hr. 12 mm, LEPENÉ NA MUR. PENU DRYFIX
	ŽELEZOBETÓNOVÁ KONŠTRUKCIA - PODROBNE DEFINOVANÁ V ČASTI STATIKA
	FASÁDNA MINERÁLNA VLNA KNAUF SMART, hr. 200mm, λ=0,035 W/m.K, R=5,70 m².K/W
	EXTRUDOVANÝ POLYSTYREN XPS, STYRODUR 2 800 C
	TEPELNÁ IZOLÁCIA Z PIR PANELOV, λ=0,022W/m.K
	SPÁDOVÝ POLYSTYRÉN NAPR. ISOVER EPS 150S, λ=0,034W/m.K
	HYDROIZOLÁCIA
	DRVENÉ KAMENIVO, MAKADAM FR. Ø16- 32cm

POZNÁMKY:

TÁTO DUKUMENTACIA JE URČENÁ NA STAVEBNÉ POVOLENIE, NENAHRÁDZA REALIZAČNÝ PROJEKT STAVBY. V PRÍPADE NEJASNOSTI ZAVOLAŤ PROJEKTANTA RESP. DOZOR STAVBY.

±0,000 = BPV 199.00 m.n.m.

ZODPOVEDNÝ PROJEKTANT:	ING. STANISLAV NIGUT	AUTORIZÁCIA: ING. STANISLAV NIGUT	SEVERKA: S
VYPRACOVAL :	ING . LUKÁŠ IŠTOK		
INVESTOR:	comparo s.r.o. Na Močidlách 23, 040 18 Košice - Krásna		
NÁZOV A MIESTO STAVBY	DVOJDOM KATASTRÁLNE ÚZEMIE: MOKRANCE PARCELA ČÍSLO: 436/6,7,10,11, 437/24, 5893/307, 393, 6198/7 OBEC: MOKRANCE, OKRES: KOŠICE-OKOLIE	comparo can not compare comparo s.r.o. Na Močidlách 23 040 18 Košice	
DRUH PROJEKTU:	PROJEKT PRE STAVEBNÉ POVOLENIE	DÁTUM: 07/2023	PARÉ: / ČÍSLO VÝKRESU:
DRUH DOKUMENTÁCIE:	ARCHITEKTÚRA SO 01, SO 02	FORMÁT: 630x420	
OBSAH VÝKRESU :	PÔDORYS 1.NP	MIERKA: 1:50	3

DOKUMENTÁCIA PRE STAVEBNÉ POVOLENIE NENAHRÁDZA REALIZAČNÝ PROJEKT STAVBY A JE VÝLUČNÝM VLASTNÍCTVOM AUTORA